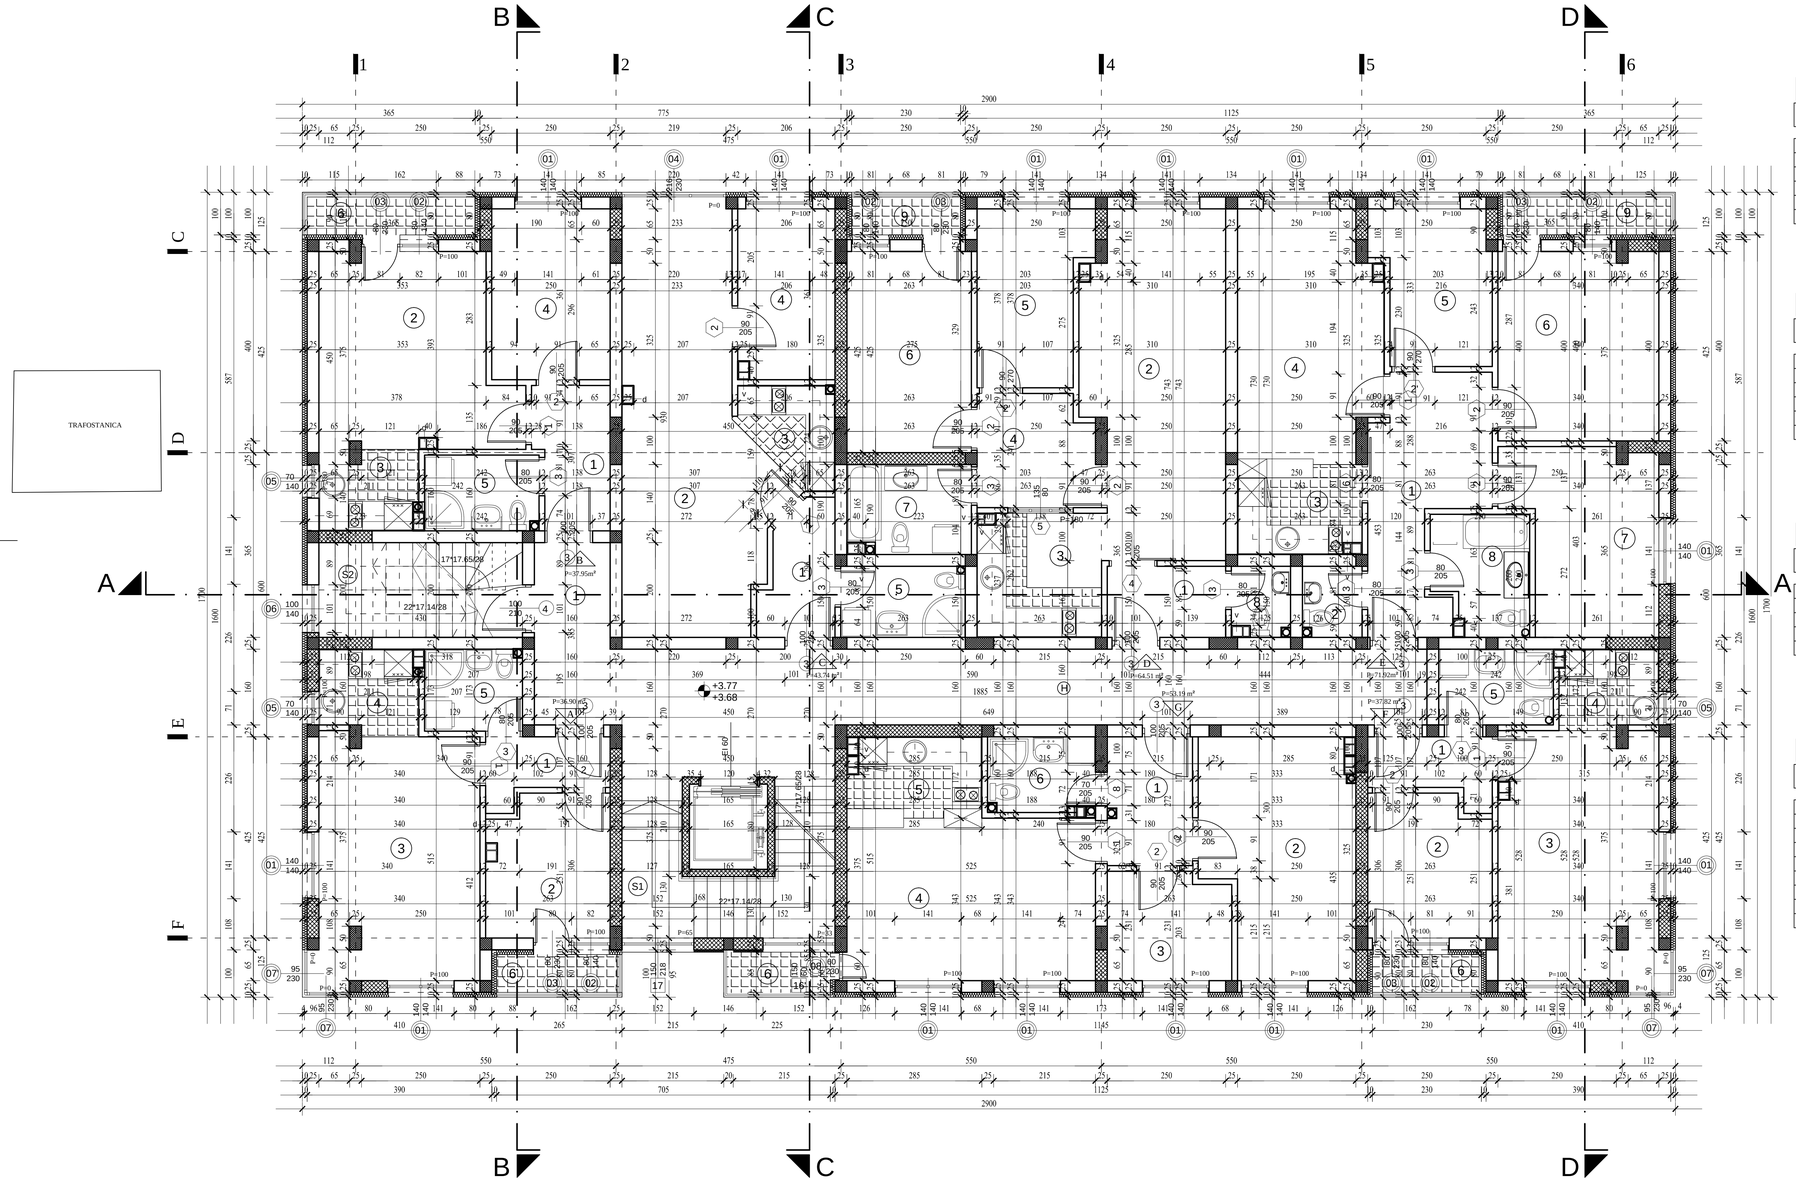

STAN A

Br.	naziv prostorije	POD	ZID	P/m 2	O/m 1
1	hodnik	kera.pločice	dispe. boja	3.14	8.50
2	soba	parket	dispe. boja	7.55	11.38
3	dne. soba sa trpe	parket	dispe. boja	17.80	18.91
4	kuhinja	kera.pločice	kera.plo./dispe.boja	3.63	7.79
5	kupatilo	kera.pločice	kera.pločice	3.58	7.60
6	terasa 50%	kera.pločice	fasadna boja	1.20	7.10
			UKUPNO	36.90	61.28

STAN B

Br.	naziv prostorije	POD	ZID	P/m 2	O/m 1
1	hodnik	kera.pločice	dispe. boja	4.61	9.46
2	dne. soba sa trpe	parket	dispe. boja	15.89	19.10
3	kuhinja	kera.pločice	kera.plo./dispe.boja	3.29	7.66
4	soba	parket	dispe. boja	9.03	12.22
5	kupatilo	kera.pločice	kera.pločice	3.87	8.04
6	terasa 50%	kera.pločice	fasadna boja	1.65	9.10
			UKUPNO	38.34	65.58

STAN C

Br.	naziv prostorije	POD	ZID	P/m 2	O/m 1
1	hodnik	kera.pločice	dispe. boja	3.98	8.82
2	dne. soba sa trpe	parket	dispe. boja	24.86	25.44
3	kuhinja	kera.pločice	kera.plo./dispe.boja	3.63	7.94
4	spavaća soba	parket	dispe. boja	7.32	11.33
5	kupatilo	kera.pločice	kera.pločice	3.95	8.26
			UKUPNO	43.74	61.79

STAN D

Br.	naziv prostorije	POD	ZID	P/m 2	O/m 1
1	hodnik	kera.pločice	dispe. boja	3.75	8.00
2	dne. soba sa trpe	parket	dispe. boja	20.55	21.30
3	kuhinja	kera.pločice	kera.plo./dispe.boja	6.79	10.50
4	hodnik	parket	dispe. boja	5.85	10.08
5	soba	parket	dispe. boja	8.16	12.56
6	soba	parket	dispe. boja	11.18	13.76
7	kupatilo	kera.pločice	kera.pločice	4.90	9.06
8	wc	kera.pločice	kera.pločice	1.78	5.50
9	lođa 75%	kera.pločice	fasadna boja	1.55	6.40
			UKUPNO	64.51	97.16

STAN E

Br.	naziv prostorije	POD	ZID	P/m 2	O/m 1
1	hodnik	kera.pločice	dispe. boja	10.85	17.64
2	wc	kera.pločice	kera.pločice	1.88	5.50
3	kuhinja	kera.pločice	kera.plo./dispe.boja	4.90	9.06
4	dne. soba sa trpe	parket	dispe. boja	15.35	17.00
5	soba	parket	dispe. boja	7.56	11.92
6	soba	parket	dispe. boja	13.54	15.40
7	soba	parket	dispe. boja	11.37	15.36
8	kupatilo	kera.pločice	kera.pločice	4.83	9.40
9	terasa 50%	kera.pločice	fasadna boja	1.64	9.10
			UKUPNO	71.92	110.38

STAN F

Br.	naziv prostorije	POD	ZID	P/m 2	O/m 1
1	hodnik	kera.pločice	dispe. boja	3.14	8.50
2	soba	parket	dispe. boja	7.65	11.38
3	dne. soba sa trpe	parket	dispe. boja	18.14	19.52
4	kuhinja	kera.pločice	kera.plo./dispe.boja	3.47	7.66
5	kupatilo	kera.pločice	kera.pločice	3.87	8.04
6	lođa 75%	kera.pločice	fasadna boja	1.55	6.40
			UKUPNO	37.82	61.50

STAN G

Br.	naziv prostorije	POD	ZID	P/m 2	O/m 1
1	hodnik	kera.pločice	dispe. boja	4.80	9.84
2	soba	parket	dispe. boja	15.17	16.96
3	soba	parket	dispe. boja	5.84	9.88
4	dne. soba sa trpe	parket	dispe. boja	18.01	17.24
5	kuhinja	kera.pločice	kera.plo./dispe.boja	4.70	9.14
6	kupatilo	kera.pločice	kera.pločice	3.60	7.56
7	terasa 75%	kera.pločice	fasadna boja	1.07	6.40
			UKUPNO	53.19	77.02

zajednicke prostorije

ozn.	naziv prostorije	vrsta poda	P/m 2	O/m 1
H	hodnik	keramicke pl.	39.99	48.60
S1	stepenište	keramicke pl.	10.40	18.60
S2	stepenište	keramicke pl.	8.60	12.60
		UKUPNO	58.99	79.80

Ukupna neto površina I sprata:	405.41
Ukupna korisna površina I sprata (neto -3%):	393.25
Ukupna bruto površina I sprata:	484.38

LEGENDA MATERIJALA

- ZIDANI ZID
- ARMIRANI BETON

STOLARIJA I BRAVARIJA

- 0 aluminijumska bravarija
- 0 crna bravarija
- 0 PVC stolarija
- 0 drvena stolarija

NAPOMENA:
Kota prizemlja ±0.00 odgovara apsolutnoj koti terena 91.72m.

APROJEKT PROJEKTIRANJE - KONSALTING - INŽENJERING		investitor: DOO "CSP" DVOROVI	
odgovorni projektant: Mirjana Erić, dipl.inž.arh.		projekat: VIŠEPORODIČNI STAMBENO-POSLOVNI OBJEKAT	
projektant faze: Mirjana Erić, dipl.inž.arh.		lokacija: Bijeljina	datum: 2019.godina / razmjera: 1:50
FAZA: ARHITEKTURA	ŠIFRA: 79-6/19	OSNOVA I SPRATA	broj lista: 4